Kosan Crisplant®

Costummer : Standard drawing

Project description : GENERAL

Drawing Number : 1000979R05

Subject : POWER/COMMUNICATION FOR CUC-Ex

Placement	:	Line voltage, freq.	: 1x85-264VAC+N+PE, 50/60Hz, 0,1kW
Speciel terms	:	Control voltage	: 8-14 VDC
Norm/standards	:	Power consumption.	:
Capsuling Class	:	Rated current	:
Ambient temperature	:	Short-circuit Ikmax.	:
Relative humidity	:	Short-circuit Ikmin.	:
Distribution system	:	Main cable	: 3 x 1.5mm²
Cubicles	:	Incoming cable	:
Fabrication year	: 2000	Outgoing cables	:

Project start	: 06. Dec. 2000	Largest page no.	: 17
Project responsible	: KHO	Total pages	: 11
Latest change	: 26. Apr. 2007		
Latest Constructor	: MBP		

Page overview

KCR1201E / 04.Oct.1994-KBF

Page	Page description	Page Additional information	Date	Construc.
1	PANEL SPECIFICATION		15.Aug.2003	MBP
2	Page overview - Index		30.Mar.2007	KCR
3	General informations		06.Sep.2006	VKV
10	INTERFACE PANEL, CUC COMMUNICATION		30.Mar.2007	KHO
11	POWER SUPPLY, INLET, OUTLET AND SCALES		30.Mar.2007	KHO
12	POWER SUPPLY, ET-IR AND ET-PT		16.Jul.2002	KHO
13	FILLING MACHINES		30.Mar.2007	KHO
14	FILLING MACHINES		30.Mar.2007	KHO
15	FILLING MACHINES		14.Aug.2001	KHO
16	FILLING MACHINES		14.Aug.2001	KHO
17	POWER SUPPLY, PALLET PLANT		30.Mar.2007	KHO

Title	Page overview - Index	Drawn 06.Dec.2000	App.	Rev.	Date	Drawing No. 1000979R05	Cont. page 3
Subject	POWER/COMMUNICATION FOR CUC-Ex	Plotted 26.Apr.2007	Eng. KHO		30.Mar.2007		Page no. 2
Project	GENERAL		Drw. KCR				

Markings on panel sign

Main supply : 1x85-264VAC+N+PE, 50/60Hz, 0,1kW

Power consumption. :

Power consumption. :

Rated current :

Short-circuit Ikmax.: Max 30 kA

General plant informations

Speciel terms :

Ambient temperature :

Relative humidity :

Supply system :

Cubicles :

Short-circuit Ikmin.:


General plant informations


Main cable : 3 x 1.5mm²

Incoming cable : Bottom

Outgoing cables : Bottom / Top

Title	General informations	Drawn 06. Dec. 2000	App.	Rev.	Date	Kosan Crisplant®	Drawing No. 1000979R05	Cont. page 10
Subject	POWER/COMMUNICATION FOR CUC-Ex	Plotted 26. Apr. 2007	Eng. KHO		06. Sep. 2006			Page no. 3
Project	GENERAL		Drw. VKV					

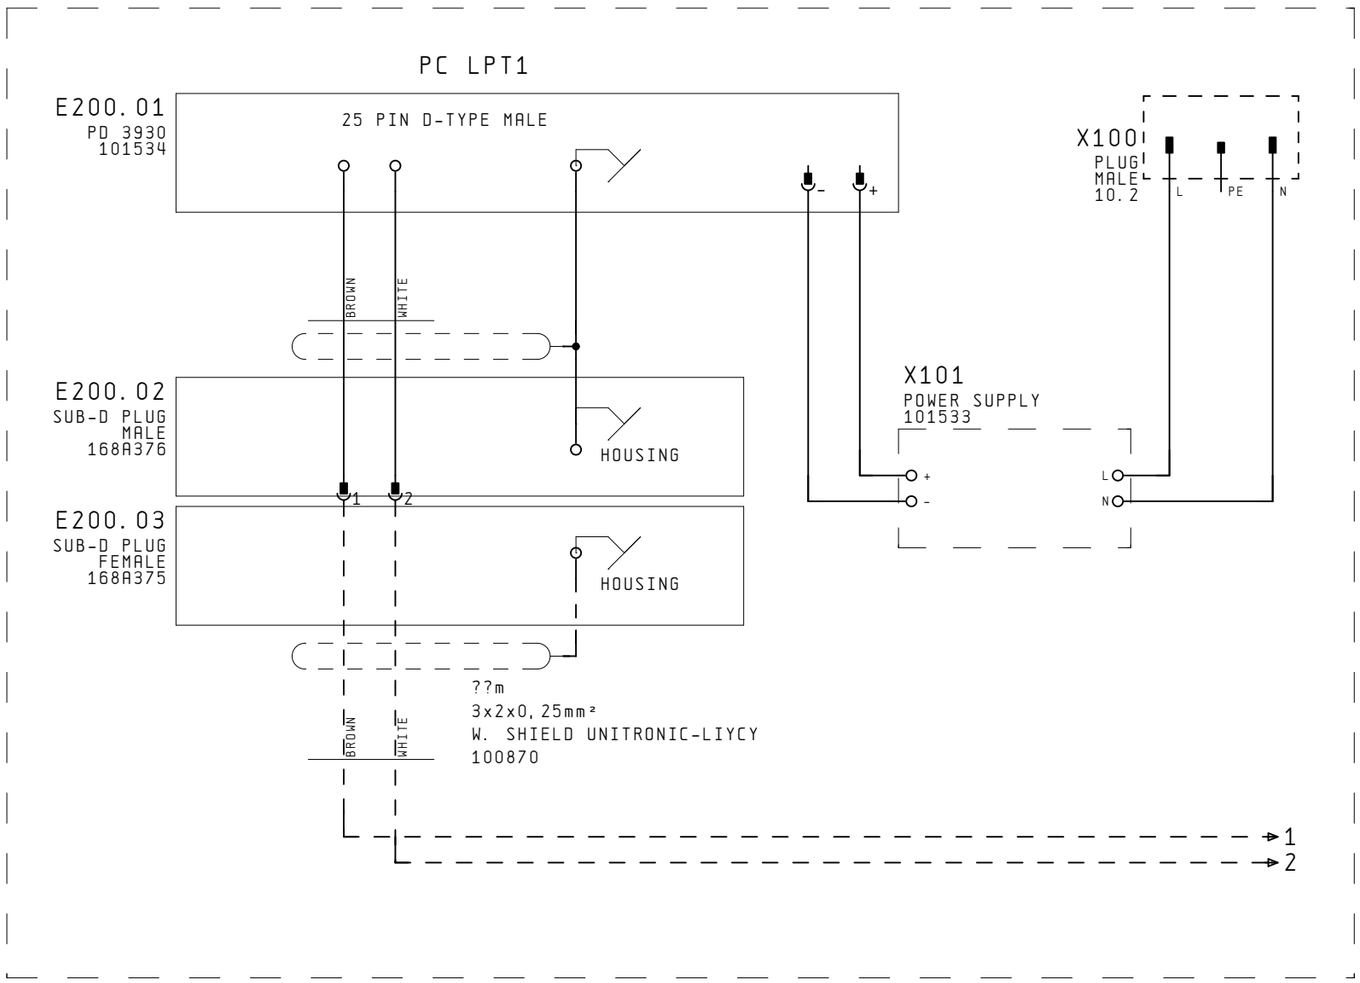

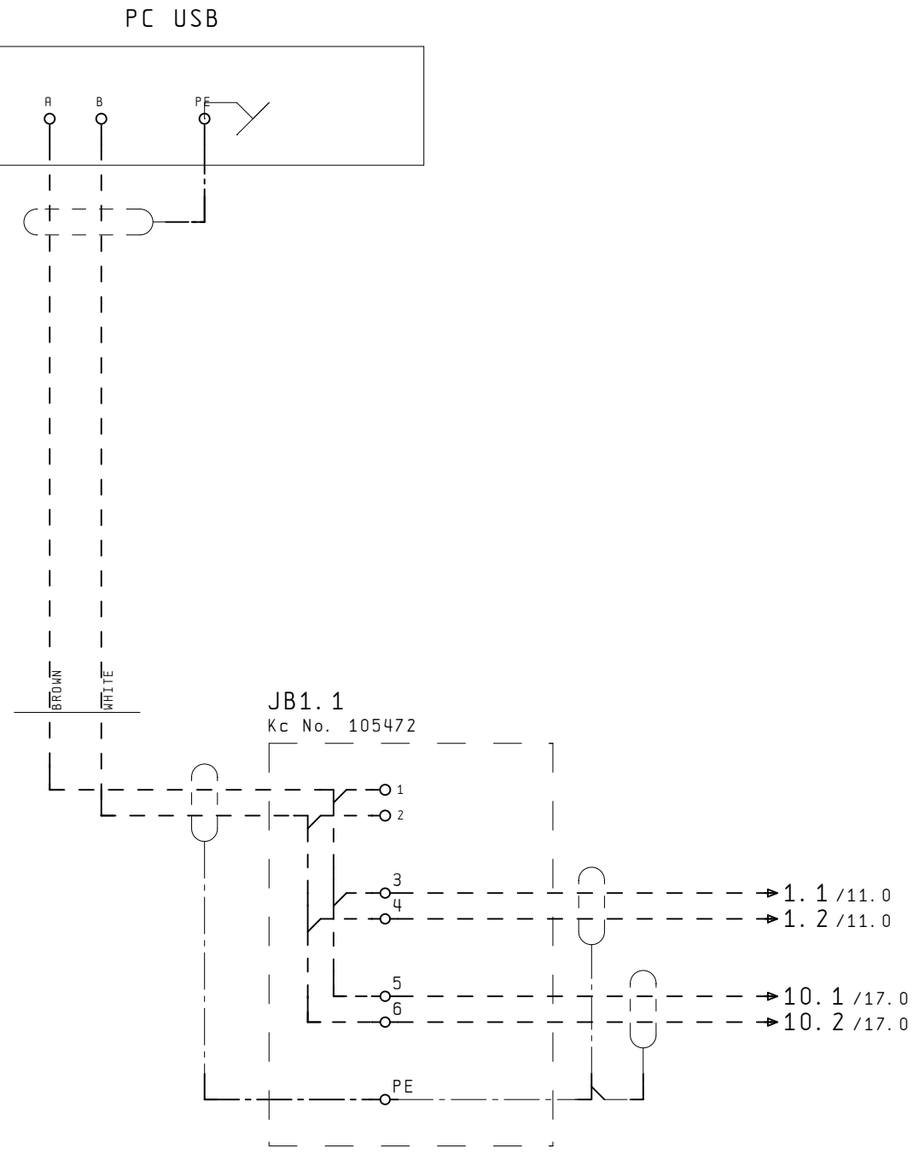


PC System
Data collection
OLD VERSION
(Option)

PC System
USB
Data collection
(Option)

Junction Boks
Data collection
(Option)


3

Title	INTERFACE PANEL, CUC COMMUNICATION	Drawn 06. Dec. 2000	App.	Rev.	Date	Kosan Crisplant®	Drawing No. 1000979R05	Cont. page 11
Subject	POWER/COMMUNICATION FOR CUC-Ex		Eng. KHO		26. Apr. 2007			
Project	GENERAL	Plotted 26. Apr. 2007	Drw. KHO					Page no. 10

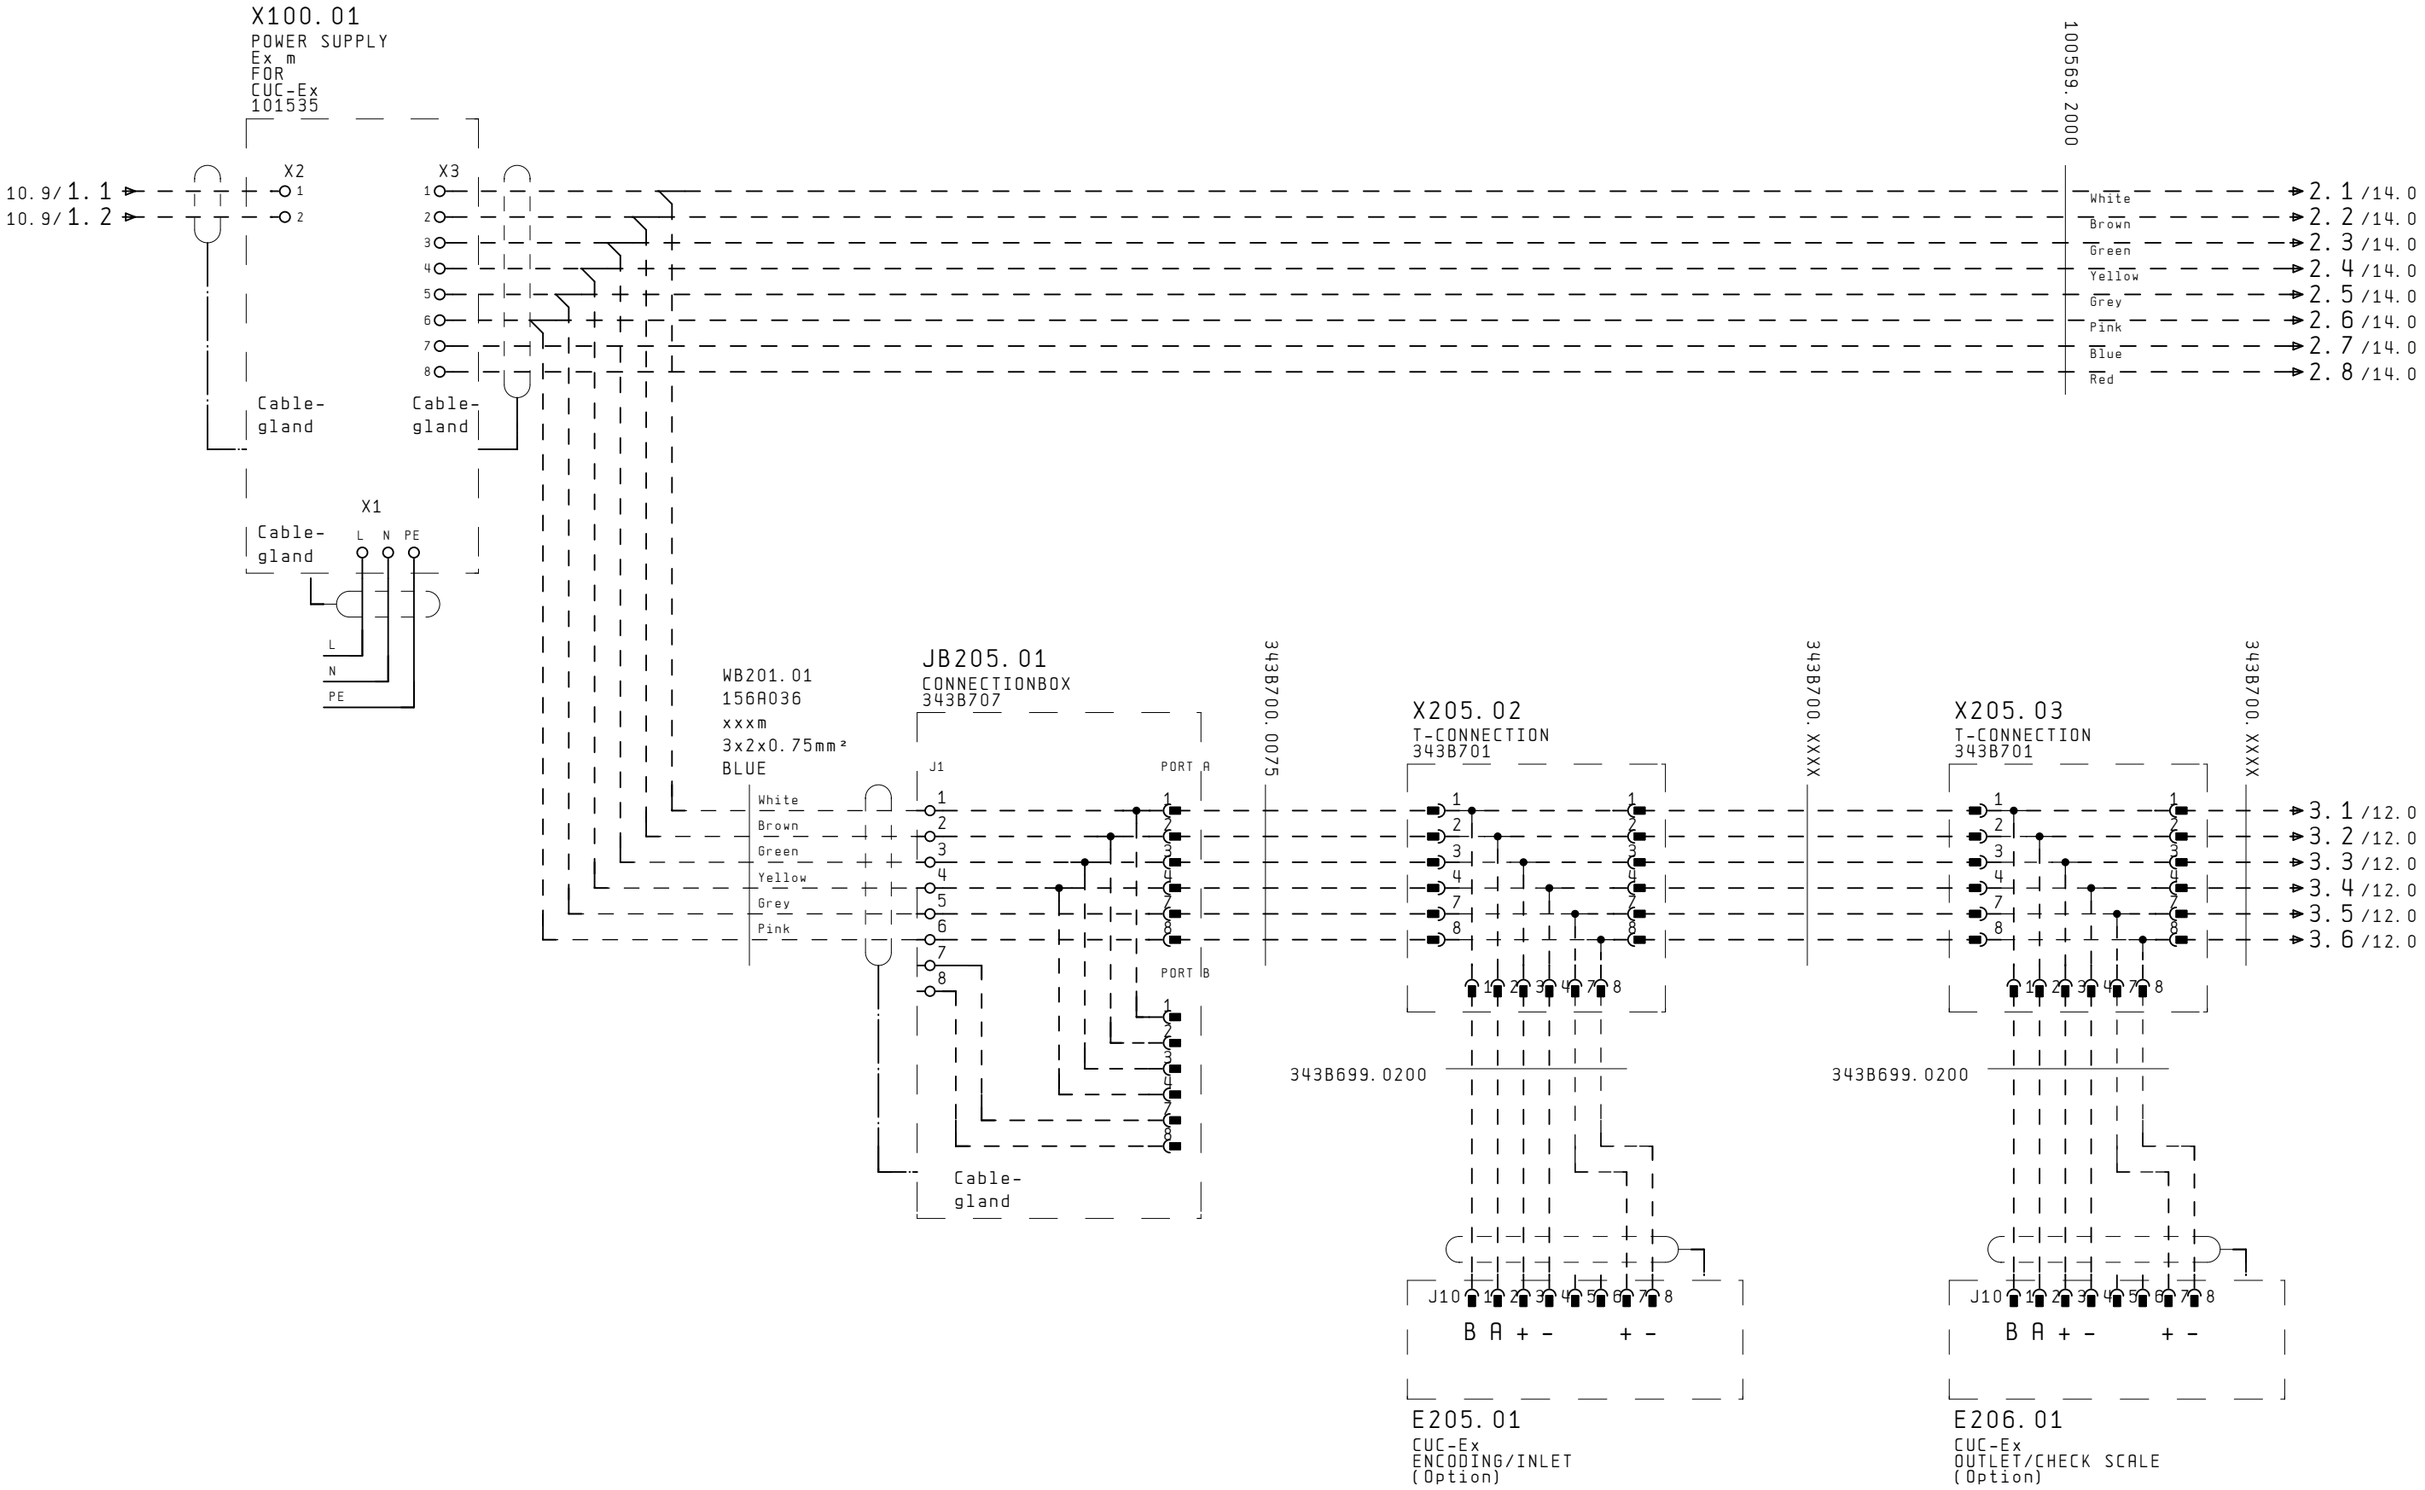


Title	POWER SUPPLY, INLET, OUTLET AND SCALES	Drawn 06. Dec. 2000	App.	Rev.	Date	Kosan Crisplant®	Drawing No. 1000979R05	Cont. page 12
Subject	POWER/COMMUNICATION FOR CUC-Ex	Plotted 26. Apr. 2007	Eng. KHO		26. Apr. 2007			Page no. 11
Project	GENERAL		Drw. KHO					

0	1	2	3	4	5	6	7	8	9

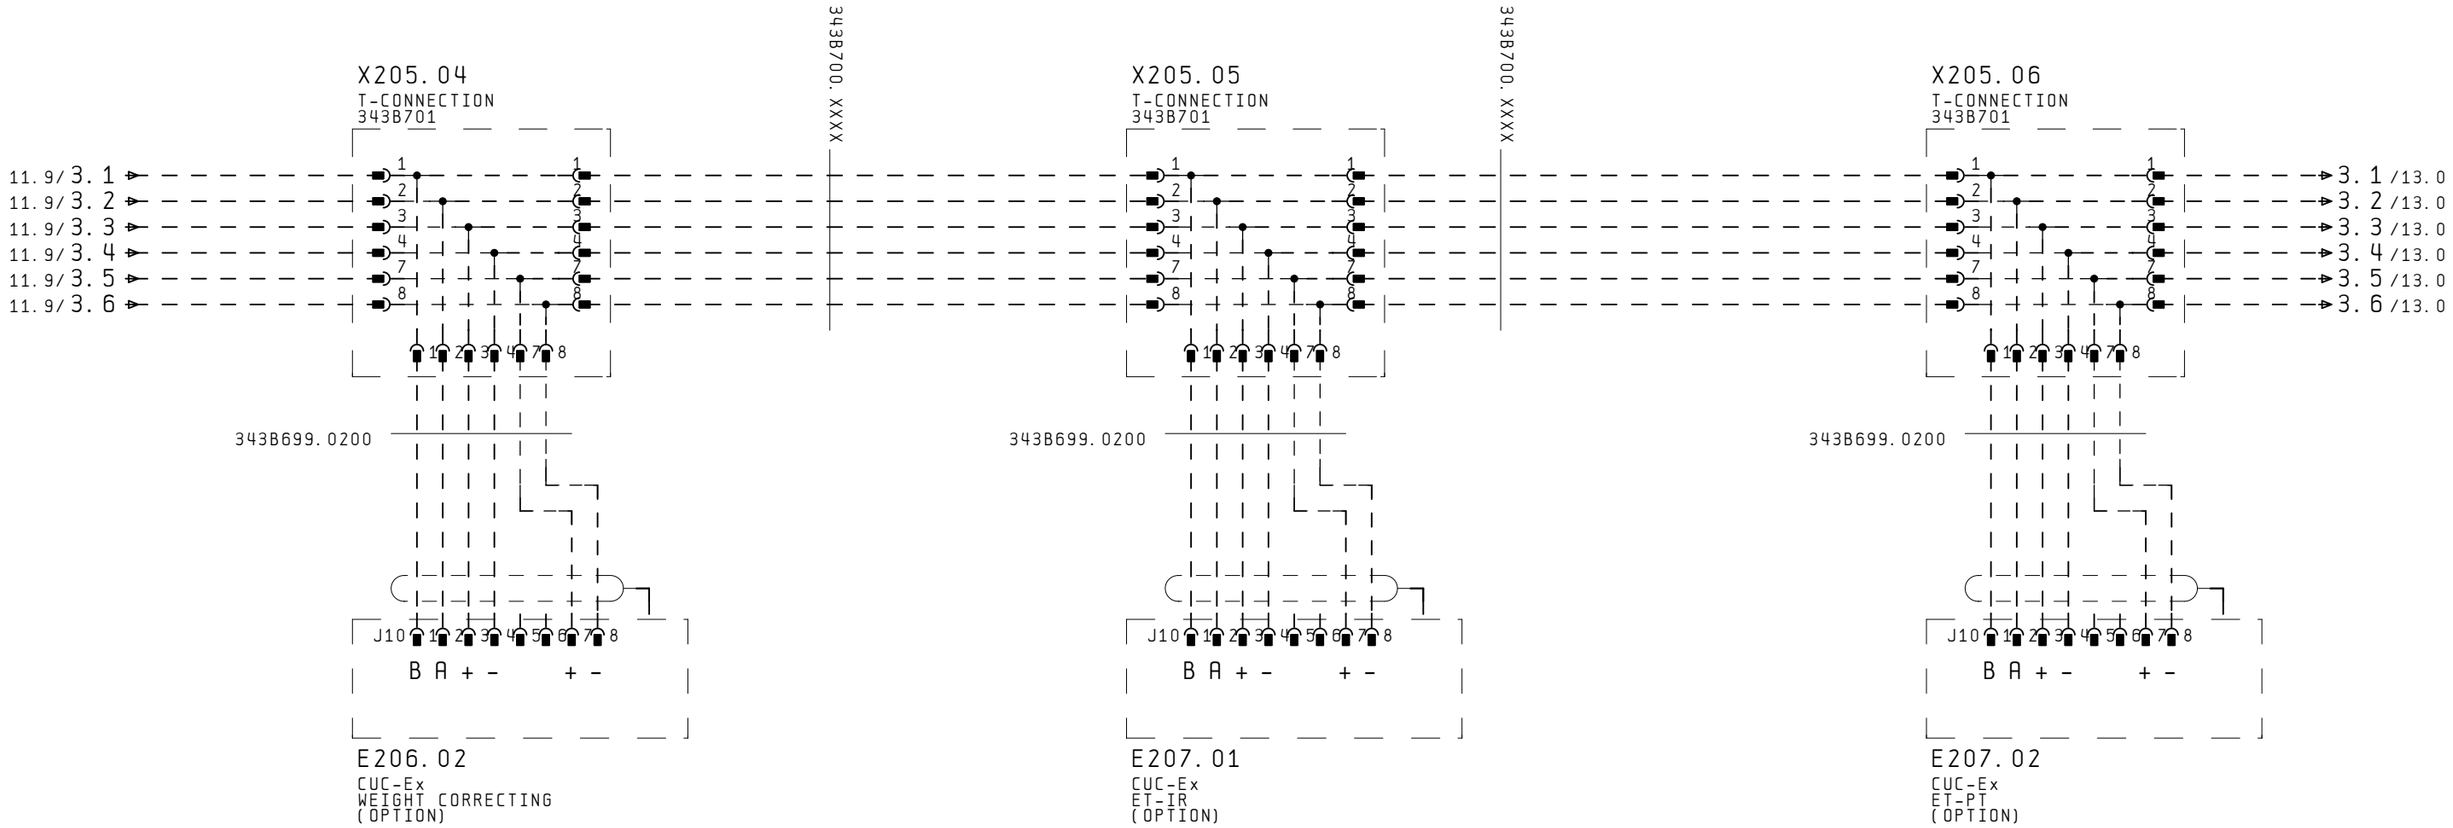


11


Title	POWER SUPPLY, ET-IR AND ET-PT	Drawn 06. Dec. 2000	App.	Rev.	Date	Kosan Crisplant®	Drawing No. 1000979R05	Cont. page 13
Subject	POWER/COMMUNICATION FOR CUC-Ex		Eng. KHO		18. Apr. 2007			Page no. 12
Project	GENERAL	Plotted 26. Apr. 2007	Drw. KHO					

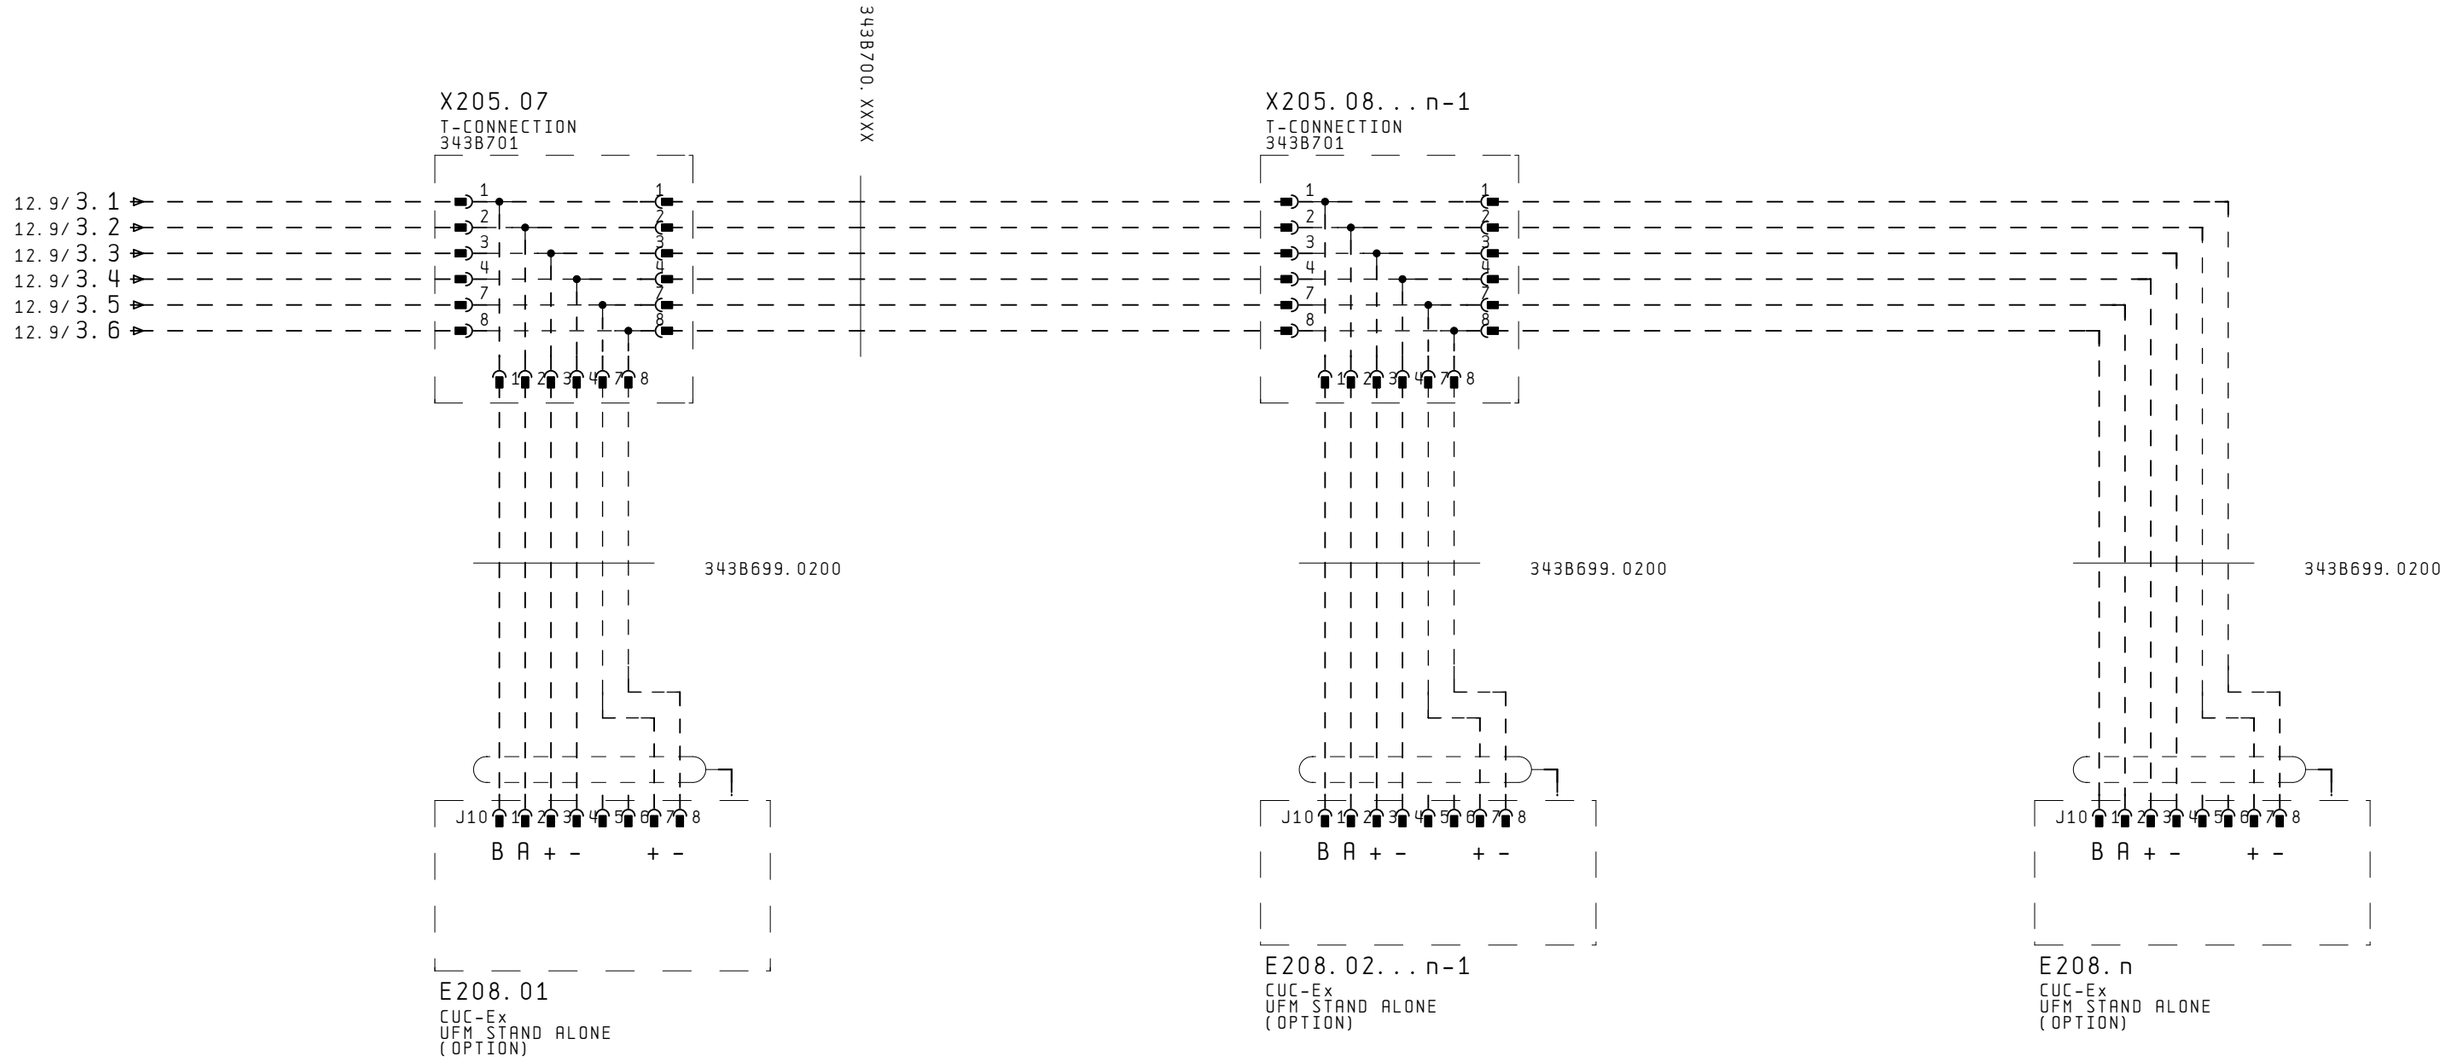

n = number of fillingmachines

Title	FILLING MACHINES	Drawn 06. Dec. 2000	App.	Rev.	Date	Kosan Crisplant®	Drawing No. 1000979R05
Subject	POWER/COMMUNICATION FOR CUC-Ex	Plotted 26. Apr. 2007	Eng. KHO		18. Apr. 2007		Cont. page 14
Project	GENERAL		Drw. KHO				Page no. 13

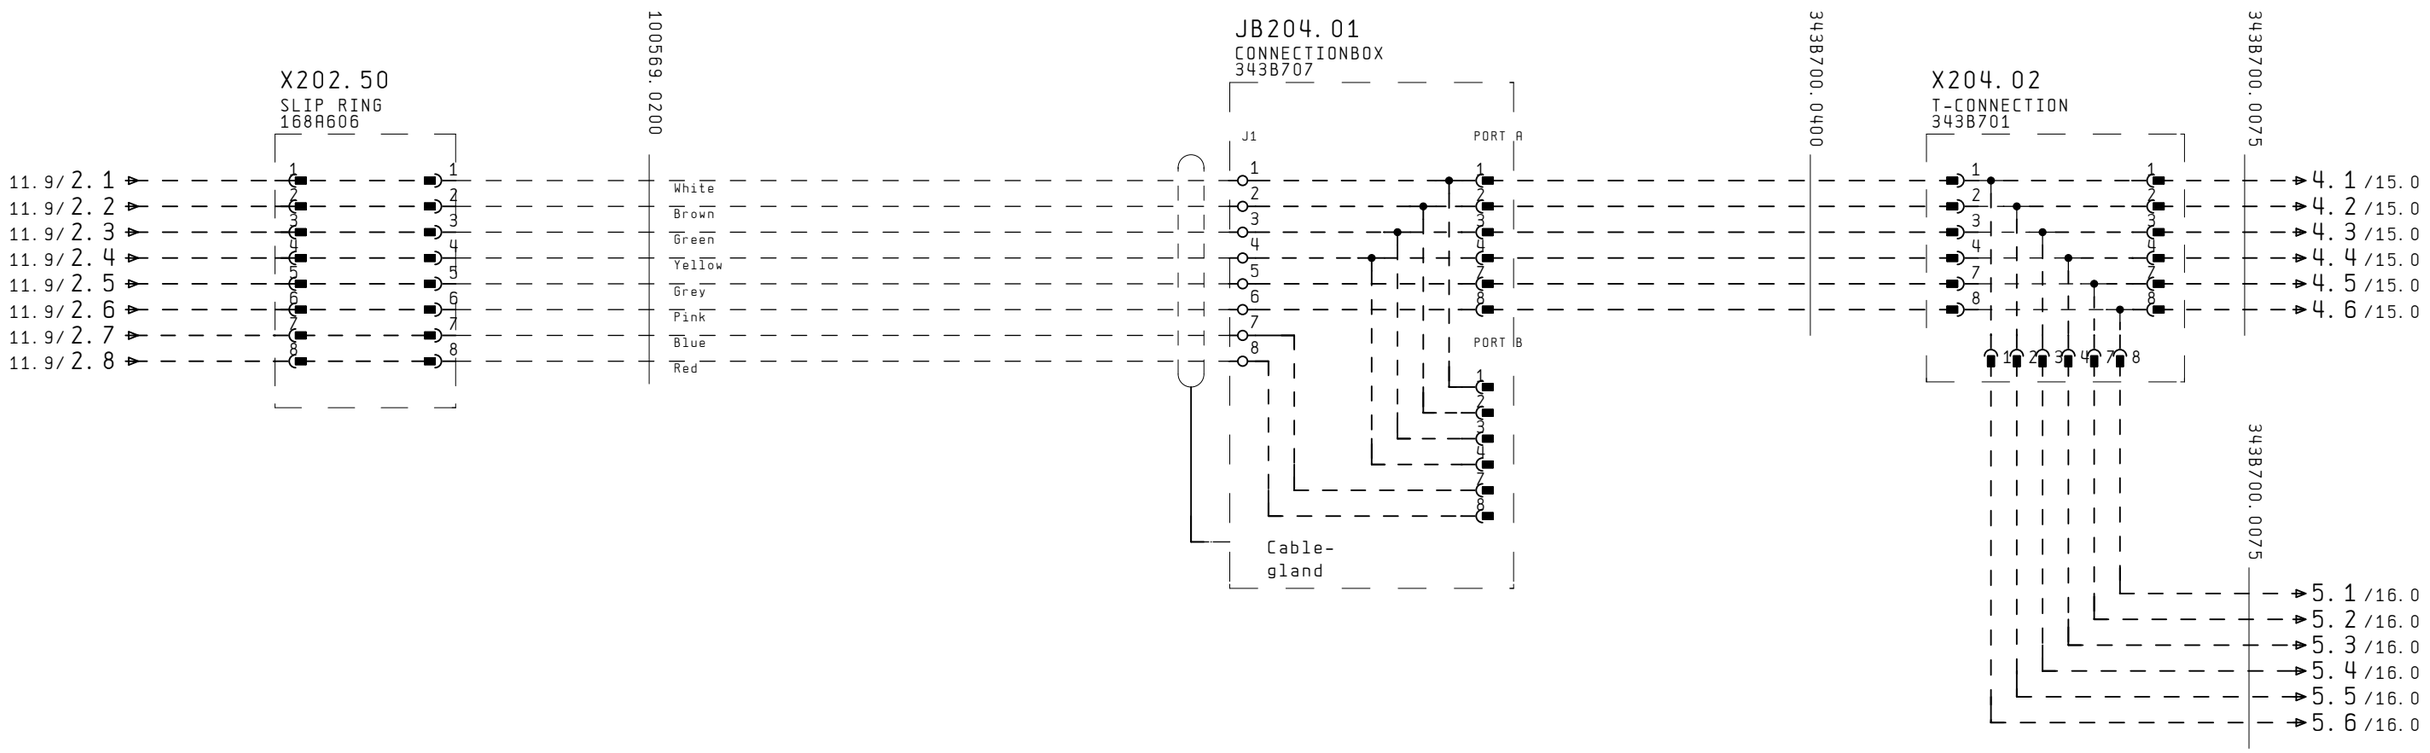

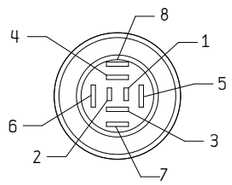


MODEL 830

13

Title	FILLING MACHINES	Drawn	06. Dec. 2000	App.		Rev.	Date	Drawing No.	Cont. page 15
Subject	POWER/COMMUNICATION FOR CUC-Ex			Eng.	KHO		18. Apr. 2007	1000979R05	
Project	GENERAL	Plotted	26. Apr. 2007	Drw.	KHO				Page no. 14


Kosan Crisplant®

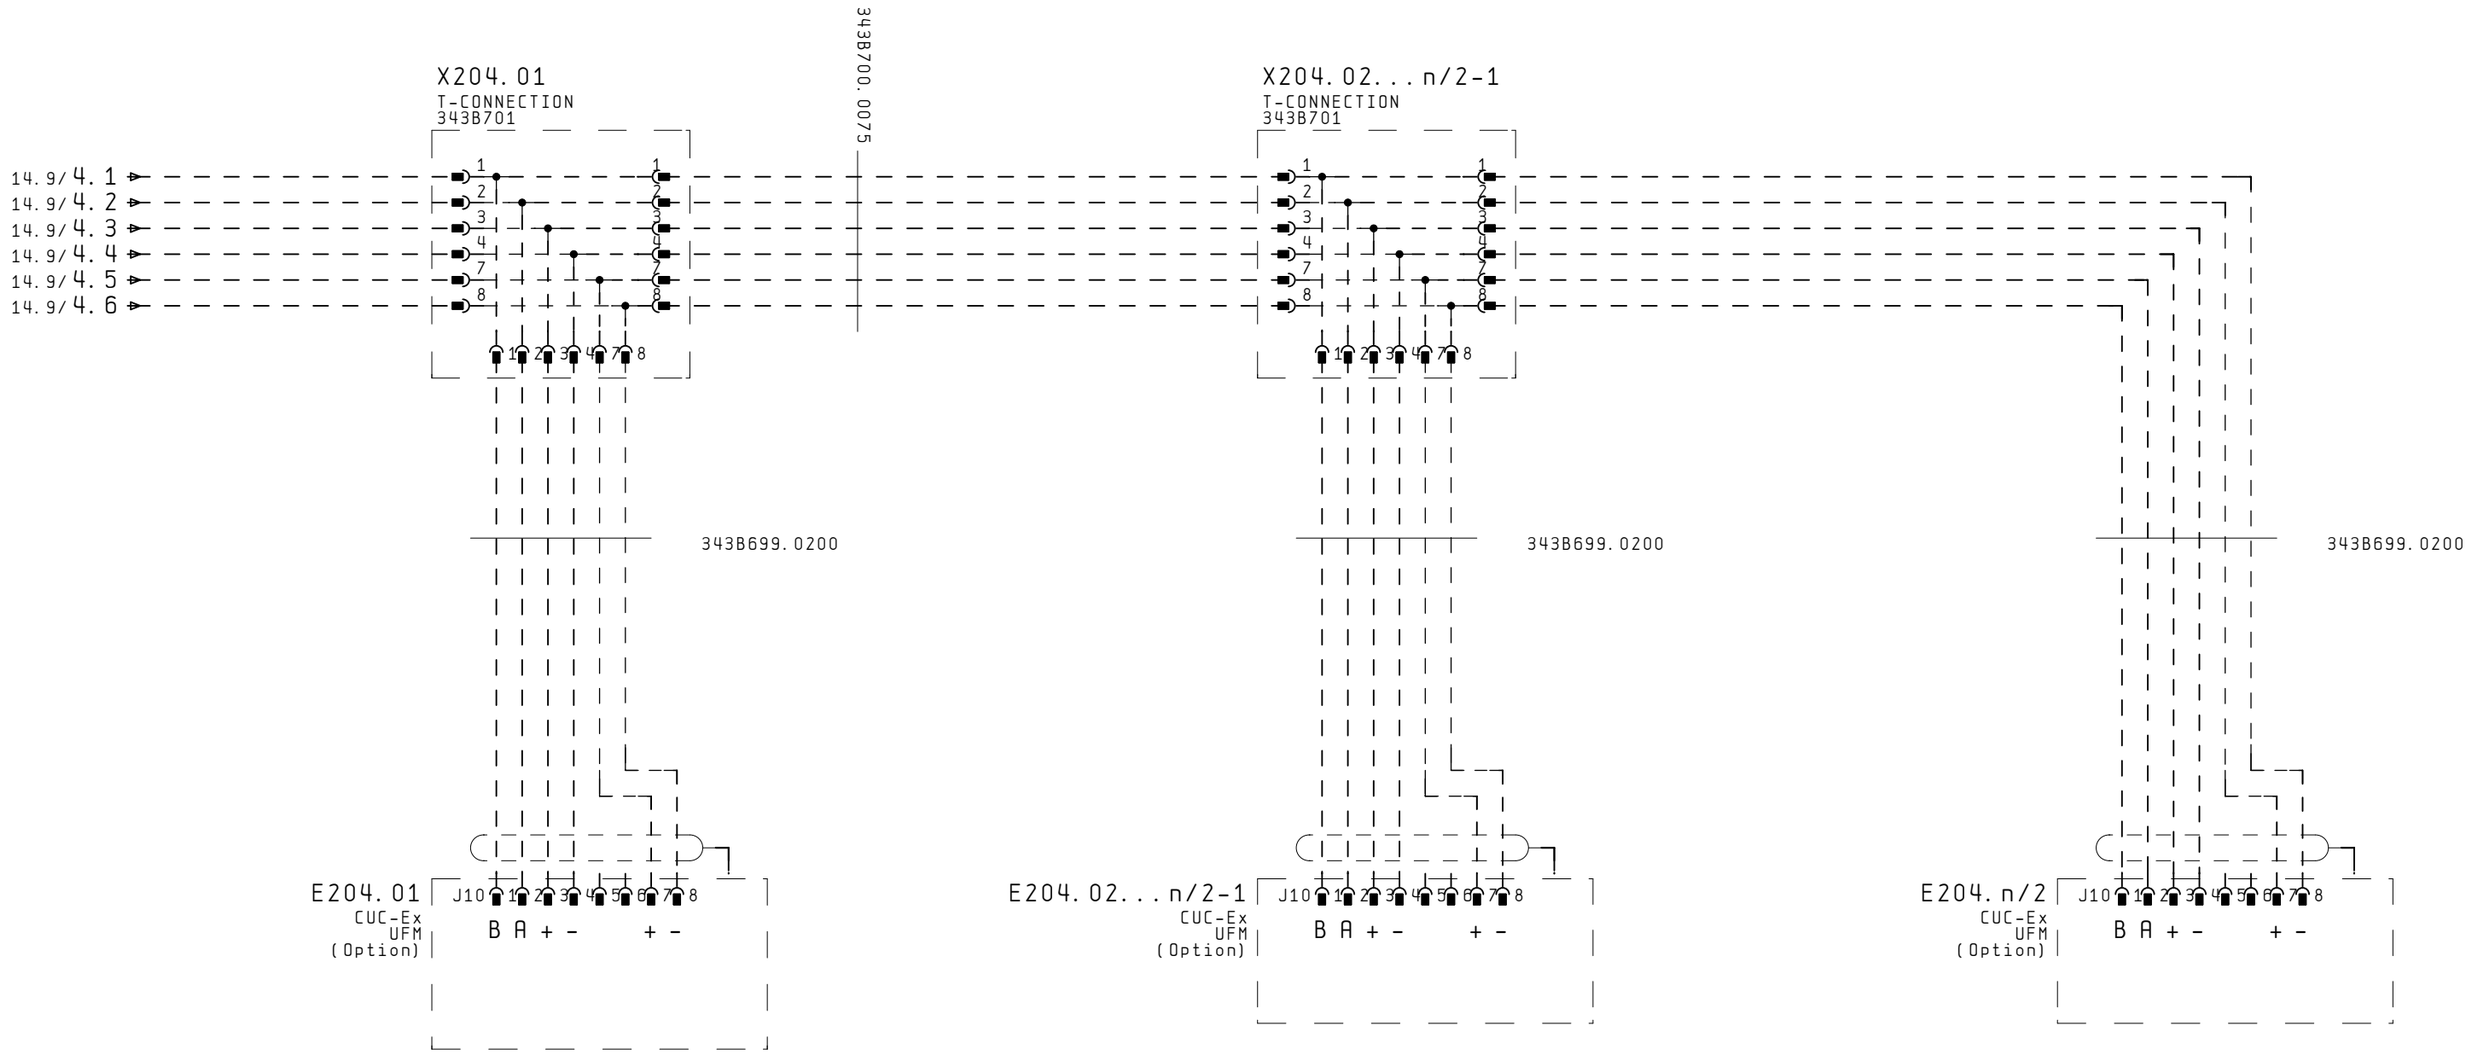

14

n = number of fillingmachines


Title	FILLING MACHINES	Drawn 06. Dec. 2000	App.	Rev.	Date	Kosan Crisplant®	Drawing No. 1000979R05	Cont. page 16
Subject	POWER/COMMUNICATION FOR CUC-Ex	Plotted 26. Apr. 2007	Eng. KHO		18. Apr. 2007			Page no. 15
Project	GENERAL		Drw. KHO					

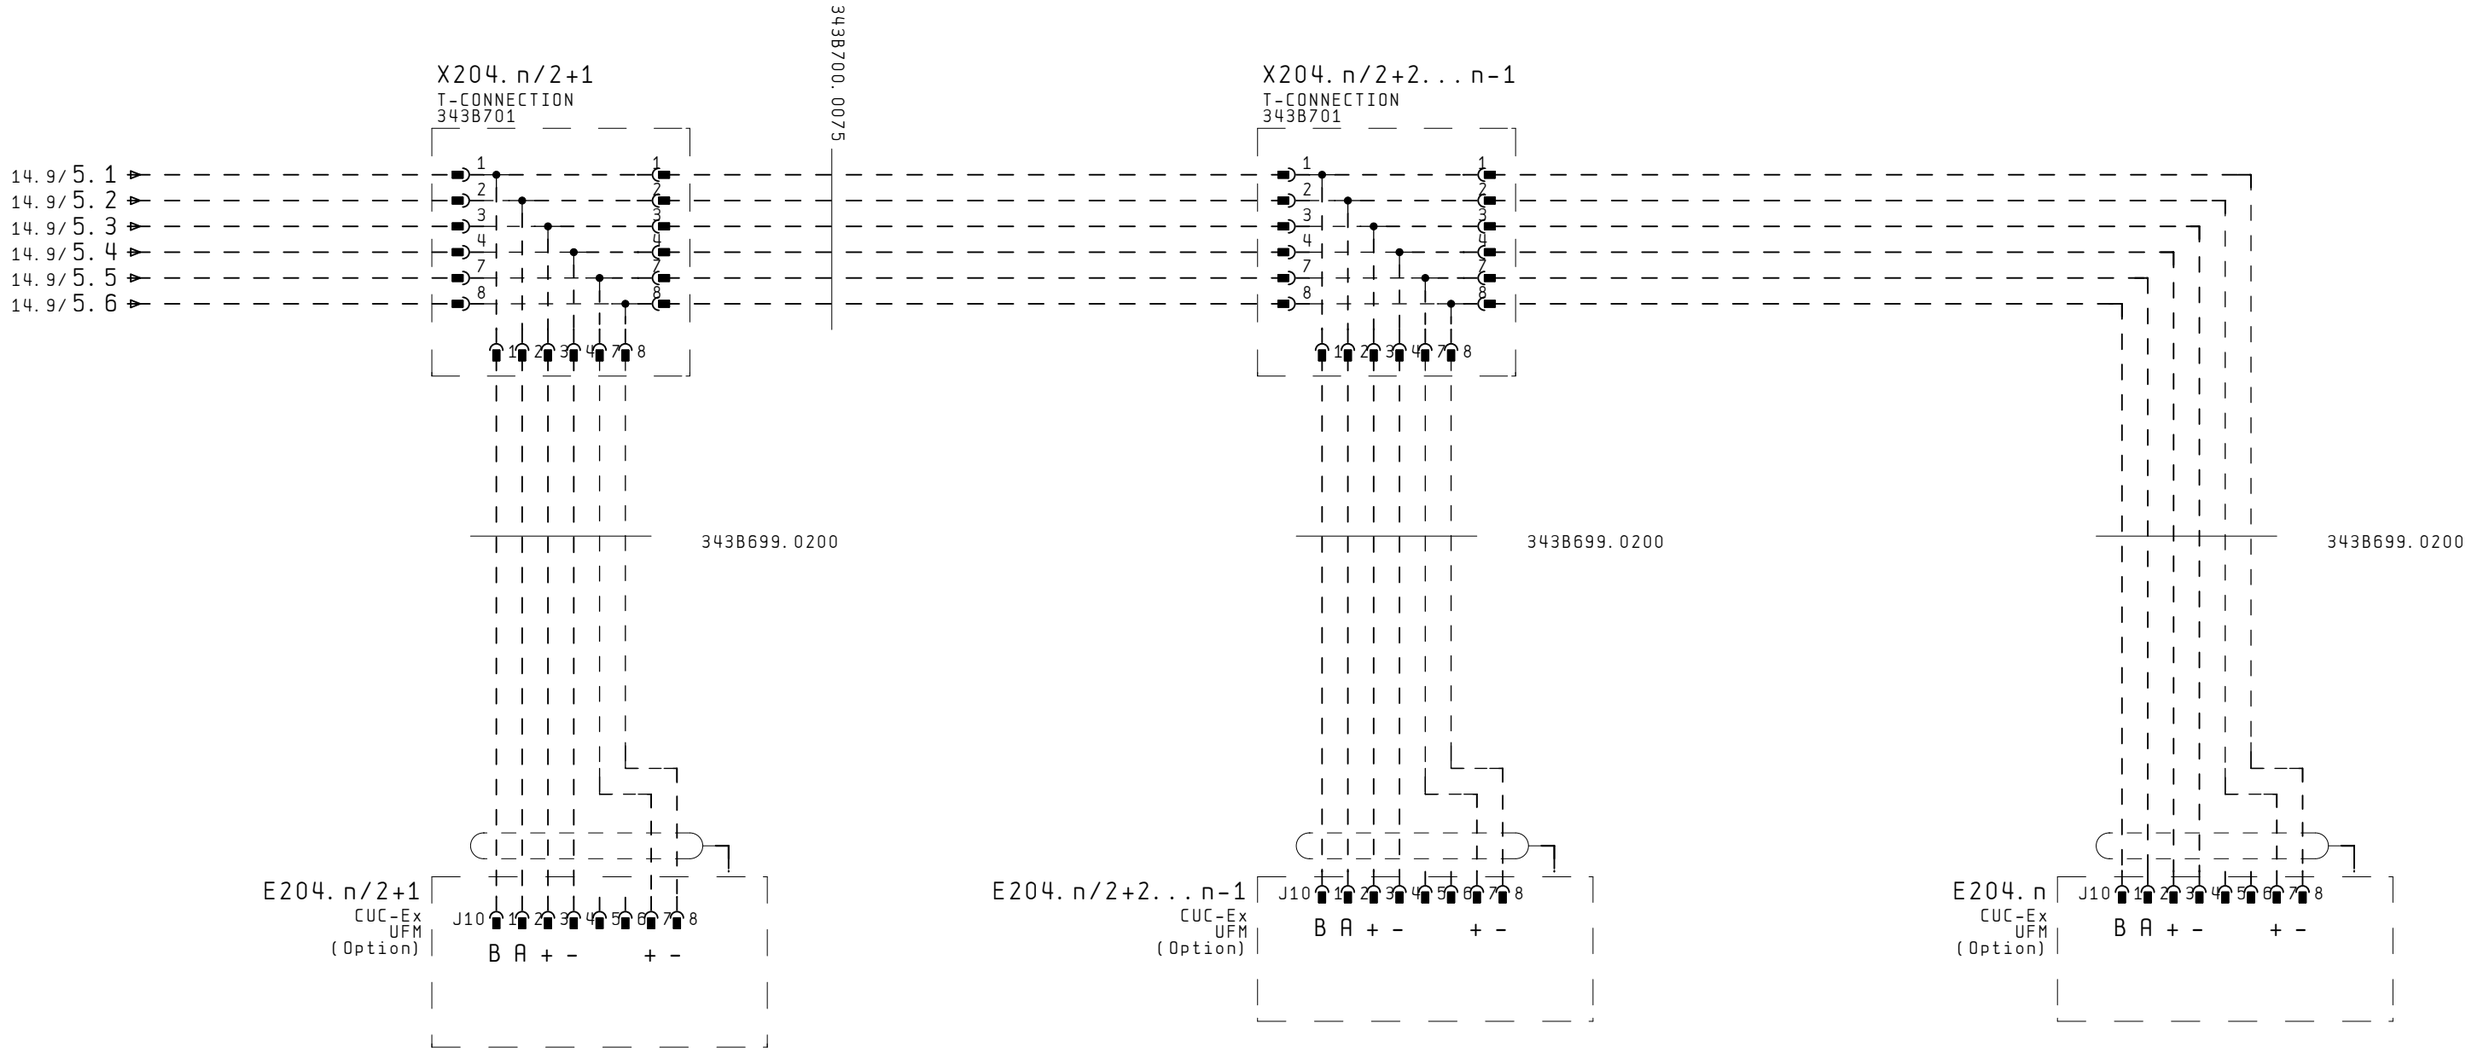

15

n = number of fillingmachines

Title	FILLING MACHINES	Drawn 06. Dec. 2000	App.	Rev.	Date	Kosan Crisplant®	Drawing No. 1000979R05	Cont. page 17
Subject	POWER/COMMUNICATION FOR CUC-Ex	Plotted 26. Apr. 2007	Eng. KHO		18. Apr. 2007			Page no. 16
Project	GENERAL		Drw. KHO					

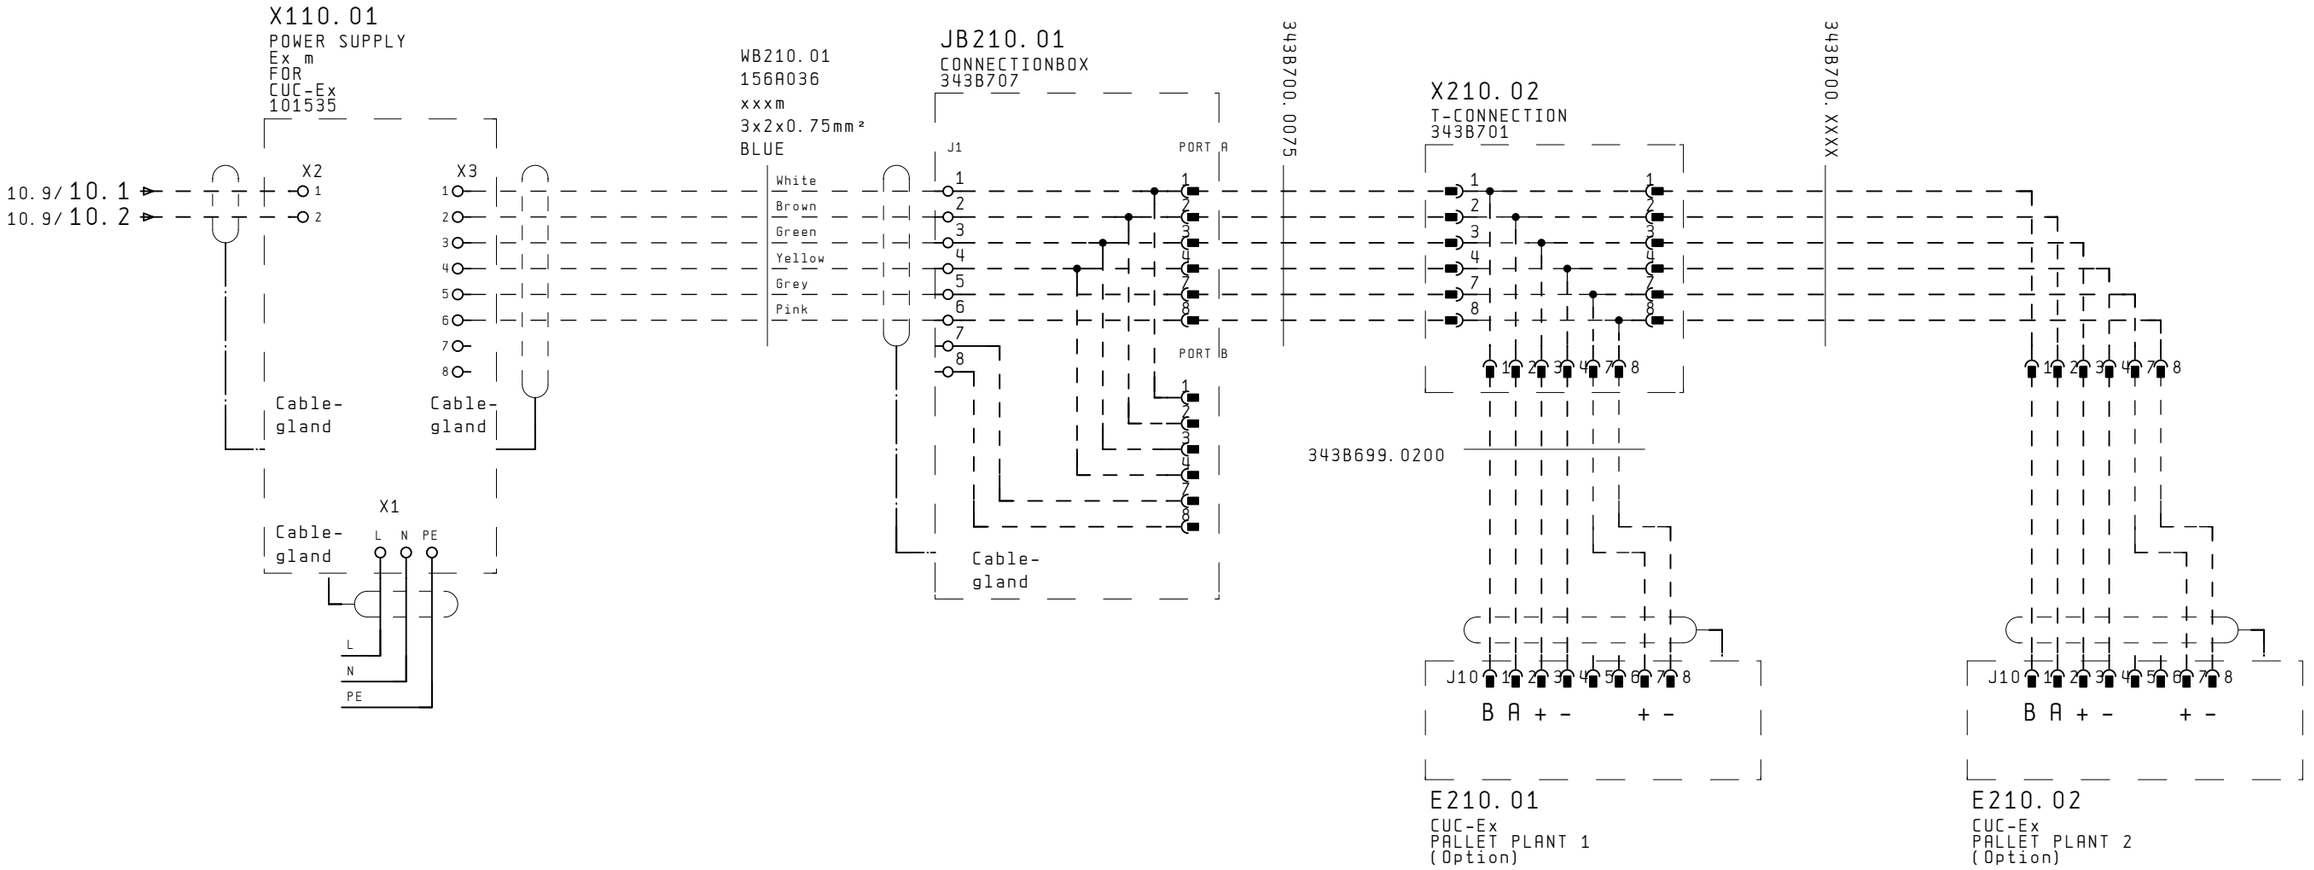

Title	POWER SUPPLY, PALLET PLANT	Drawn 06. Dec. 2000	App.	Rev.	Date	Kosan Crisplant®	Drawing No. 1000979R05	Cont. page
Subject	POWER/COMMUNICATION FOR CUC-Ex	Plotted 26. Apr. 2007	Eng. KHO		26. Apr. 2007			Page no. 17
Project	GENERAL		Drw. KHO					